


MITTAKAAVA 1:100

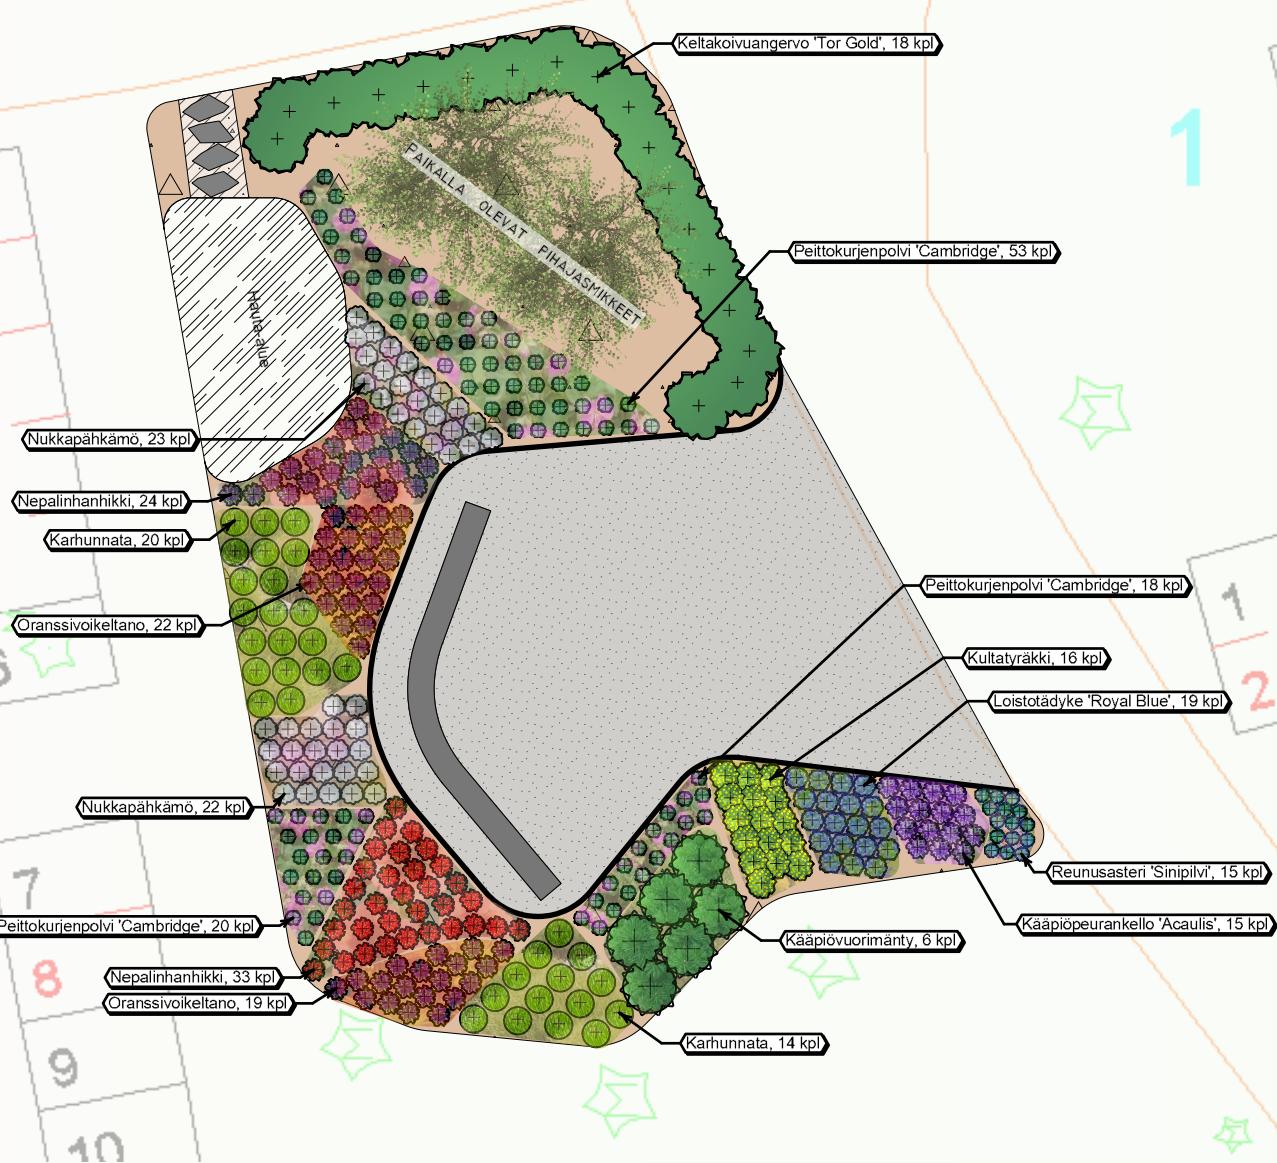

KARHUNNATA,
FESTUCA GAUTIERI
AURINKO - PUOLIVARJO, LÄPÄISEVÄ,
NIUKKA - TAI KESKIRAVINTEINEN
KORKEUS X HALKASIJJA:
15 CM X 40 CM
ISTUTUSVÄLI: 40 CM
KPL-MÄÄRÄ: 34 KPL



KELTAKOIVUANGEROV,
SPIRAEA BETULIFOLIA 'TOR GOLD'
AURINKO - PUOLIVARJO
KUIVA TAI TUORE,
KESKIRAVINTEINEN
KORKEUS X HALKASIJJA:
100 CM X 90 CM
KUKINNAN VÄRI: VALKOINEN, 6-7
ISTUTUSVÄLI: 60 CM
KPL-MÄÄRÄ: 18 KPL



KULTATYRÄKKI,
EUPHORBIA POLYCHROMA
AURINKO - KUIVA, KESKIRAVINTEINEN,
LÄPÄISEVÄ, KALKITTU
KORKEUS X HALKASIJJA:
40 CM X 40 CM
KUKINNAN VÄRI: KELTAINEN, 5-6
ISTUTUSVÄLI: 30 CM
KPL-MÄÄRÄ: 16 KPL



KÄÄPIÖPEURANKELLO 'ACAU LIS',
CAMPANULA GLomerata 'ACAU LIS'
AURINKO - PUOLIVARJO
KUIVA TAI TUORE,
KESKIRAVINTEINEN
KORKEUS X HALKASIJJA:
30 CM X 30 CM
KUKINNAN VÄRI: SINIVIOLETTI, 6-7
ISTUTUSVÄLI: 30 CM
KPL-MÄÄRÄ: 15 KPL



KÄÄPIÖVUORIMÄNTY,
PINUS MUGO 'PUMILIO'
AURINKO - PUOLIVARJO
KUIVA TAI TUORE,
NIUKKARAVINTEINEN, LÄPÄISEVÄ
KORKEUS X HALKASIJJA:
100 CM X 70 CM
ISTUTUSVÄLI: 70 CM
KPL-MÄÄRÄ: 6 KPL



LOISTOTÄDYKE 'ROYAL BLUE',
VERONICA AUSTIACA SSP. TEUCRIUM 'ROYAL BLUE'
AURINKO - PUOLIVARJO, TUORE TAI KUIVAKO,
HYVIN VETTÄ LÄPÄISEVÄ, KESKIRAVINTEINEN
KORKEUS X HALKASIJJA:
35 CM X 30 CM
KUKINNAN VÄRI: SININEN, 6-7
ISTUTUSVÄLI: 30 CM
KPL-MÄÄRÄ: 19 KPL



NEPALINHANHIKI,
POTENTILLA NEPALENSIS
AURINKO - PUOLIVARJO, TUORE TAI KUIVAKO,
KESKИ - TAI NIUKKARAVINTEINEN,
LÄPÄISEVÄ HIEKKAMULTAMA
KORKEUS X HALKASIJJA:
30 CM X 30 CM
KUKINNAN VÄRI: PUNAINEN, 7-8
ISTUTUSVÄLI: 30 CM
KPL-MÄÄRÄ: 57 KPL



NUKKAPÄHKÄMÖ,
STACHYS BYZANTINA
AURINKO - PUOLIVARJO, LÄPÄISEVÄ,
NIUKKARAVINTEINEN HIEKKAMAA
KORKEUS X HALKASIJJA:
30 CM X 30 CM
KUKINNAN VÄRI: HARMAANVIOLETTI, 6-7
ISTUTUSVÄLI: 30 CM
KPL-MÄÄRÄ: 45 KPL



ORANSSIVOIKELTANO,
HIERACIUM AURANTIACUM
AURINKO - PUOLIVARJO, KUIVA TAI PUOLIKUIVA,
NIUKKARAVINTEINEN JA HIEKKAPITOINEN
KORKEUS X HALKASIJJA:
30 CM X 30 CM
KUKINNAN VÄRI: ORANSSI, 6-7
ISTUTUSVÄLI: 30 CM
KPL-MÄÄRÄ: 41 KPL



PEITTOKURJENPOLVI 'CAMBRIDGE',
GERANIUM X CANTABRIGIENSE 'CAMBRIDGE'
AURINKO - VARJO
KUIVA JA LÄPÄISEVÄ,
NIUKKARAVINTEINEN
KORKEUS X HALKASIJJA:
20 CM X 20 CM
KUKINNAN VÄRI: VAALEANPUNAINEN, 6-7
ISTUTUSVÄLI: 30 CM
KPL-MÄÄRÄ: 91 KPL



REUNUASTERI 'SINIPILVI',
ASTER DUMOSUS 'SINIPILVI'
AURINKO - PUOLIVARJO, LÄPÄISEVÄ,
KUIVAKO TAI TUORE, KESKIRAVINTEINEN
KORKEUS X HALKASIJJA:
30 CM X 20 CM
KUKINNAN VÄRI: SININEN, 8-10
ISTUTUSVÄLI: 20 CM
KPL-MÄÄRÄ: 15 KPL



KASVEJA YHTEENSÄ = 357

SUUNNITELMA TOIVONLEHDON KASVILLISUUDELLE